


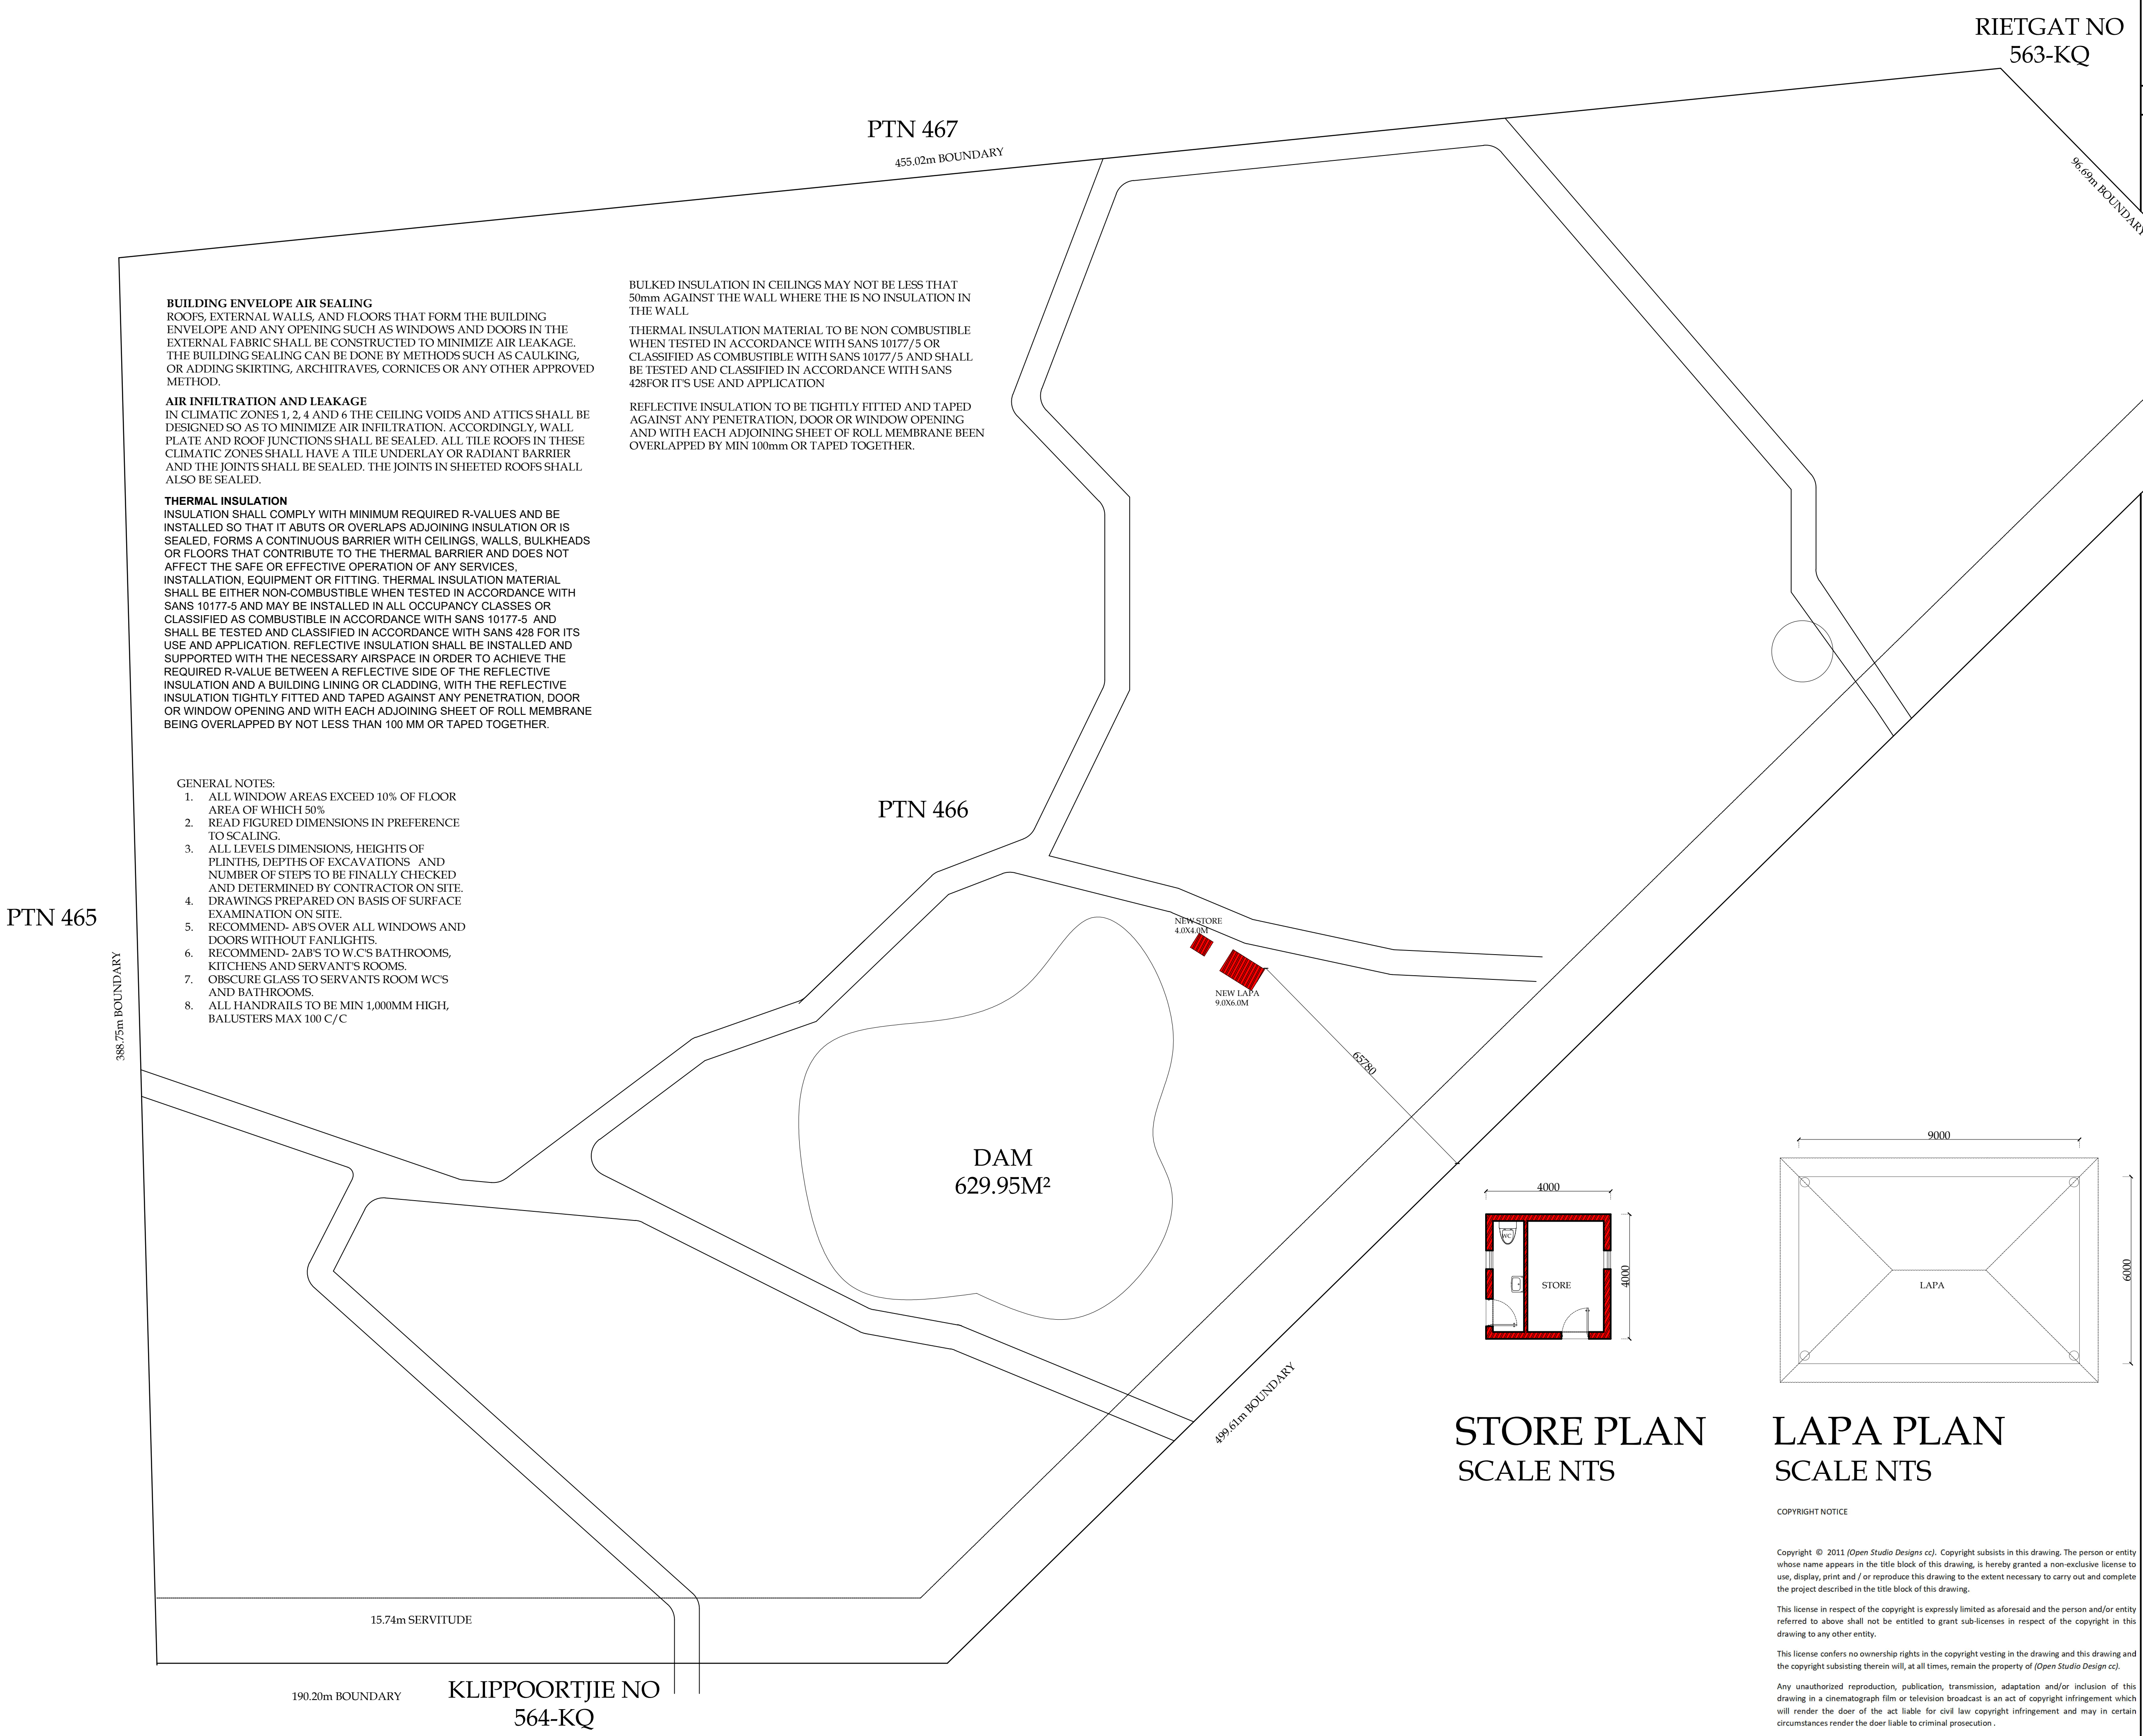

SITE DEVELOPMENT PLAN
SCALE 1:750

RIETGAT NO
563-KQ

SITE AREA13 9798m²

AREA SCHEDULE

NEW LAPA	=	54.00m²
NEW STORE	=	16.00m²
NEWAREA:		70.00m²

COVERAGE:
PROVIDED0.05 %

FAR:
PROVIDED0.05

GENERAL NOTES:

QUALITY OF ALL MATERIALS AND WORKMANSHIP TO COMPLY WITH THE RELEVANT S.A.B.S. SPECIFICATION AND SHALL COMPLY WITH THE MINIMUM STANDARD SPECIFIED IN THE STANDARD PREAMBLES IN THE BILL OF QUANTITIES OR, IN THE ABSENCE OF A BILL OF QUANTITIES, AVAILABLE FOR PERUSAL AT THE OFFICES OF THE ARCHITECTS. THE CONTRACTOR IS RESPONSIBLE FOR CORRECT SETTING OUT OF THE BUILDINGS, ALL EXTERNAL AND ALL INTERNAL WALLS WITH PARTICULAR REFERENCE TO BOUNDARIES, BUILDING LINES, ETC.

THE CONTRACTOR IS TO VERIFY LEVELS, HEIGHTS AND DIMENSIONS ON SITE AND TO CHECK SAME AGAINST THE DRAWINGS BEFORE PUTTING ANY WORK IN HAND. ANY DISCREPANCIES FROM THE THEORETICAL TO BE BROUGHT TO THE ARCHITECT'S ATTENTION.

THE CONTRACTOR AND ALL SUB-CONTRACTORS ARE TO CHECK THE DETAILS SHOWN ON THIS DRAWING FOR COMPLIANCE WITH STANDARDS OF BEST BUILDING PRACTICE (WHICH IS WHAT IS EXPECTED TO BE DELIVERED) WITH PARTICULAR REFERENCE TO SPECIAL REQUIREMENTS NECESSITATED BY LOCAL AND/OR ON SITE CONDITIONS AND TO REPORT ANY COMMENT TO THE ARCHITECTS.

THE CONTRACTOR IS TO LOCATE AND IDENTIFY EXISTING SERVICES ON SITE AND TO PROTECT THESE FROM DAMAGE THROUGHOUT THE DURATION OF THE WORKS.

ANY ERRORS, DISCREPANCIES OR OMISSIONS ON THIS DRAWING ARE TO BE REPORTED TO THE ARCHITECT IMMEDIATELY.

THE CONTRACTOR IS TO BUILD IN APPROVED DPC'S, WHETHER OR NOT THESE ARE SHOWN ON DRAWINGS, TO ALL EXTERNAL WALLS AT EACH FLOOR, BEAM OR PARAPET LEVEL AND TO ALL WINDOWS, DOORS, GRILLES OR OTHER OPENING IN EXTERNAL WALLS. CAVITY WALLS TO HAVE STEPPED DPC'S.

ANY QUERIES ARISING FROM THE ABOVE MUST BE REPORTED TO THE ARCHITECT FOR CLARIFICATION BEFORE ANY WORK IS PUT IN HAND.

THIS DRAWING IS NOT TO BE SCALED. FIGURES TO BE USED AT ALL TIMES. WHERE FIGURED DIMENSIONS ARE GIVEN, THIS MUST BE CONFIRMED BY THE ARCHITECT.

BURNT CLAY BRICKS IN COMPLIANCE WITH THE RELEVANT S.A.B.S. CODE ONLY SHALL BE USED UNLESS SPECIFIC APPROVAL IS OBTAINED FROM THE ARCHITECT FOR THE USE OF ALTERNATIVE TYPE OF BRICK.

PTN 468

Open Studio Designs

Architectural & Interiors

Mobile 083-306-4315
Fax-086-543-8765
openstudio.design@gmail.com

PROPOSED REVISED
SITE PLAN ON
PTN 466 OF THE FARM
KROMDRAAI 560KQ

CLIENT:

TECHNOLOGIST: REG. NO:	W JUNG-KRUGER D 0573
---------------------------	-------------------------

DATE: JULY19	DWG NO:
DRAWN: WJK	SHEET : 1 OF 1

BUILDING ENVELOPE AIR SEALING
ROOFS, EXTERNAL WALLS, AND FLOORS THAT FORM THE BUILDING ENVELOPE AND ANY OPENING SUCH AS WINDOWS AND DOORS IN THE EXTERNAL FABRIC SHALL BE CONSTRUCTED TO MINIMIZE AIR LEAKAGE. THE BUILDING SEALING CAN BE DONE BY METHODS SUCH AS CAULKING, OR ADDING SKIRTING, ARCHITRAVES, CORNICES OR ANY OTHER APPROVED METHOD.

AIR INFILTRATION AND LEAKAGE
IN CLIMATIC ZONES 1, 2, 4 AND 6 THE CEILING VOIDS AND ATTICS SHALL BE DESIGNED SO AS TO MINIMIZE AIR INFILTRATION. ACCORDINGLY, WALL PLATE AND ROOF JUNCTIONS SHALL BE SEALED. ALL TILE ROOFS IN THESE CLIMATIC ZONES SHALL HAVE A TILE UNDERLAY OR RADIANT BARRIER AND THE JOINTS SHALL BE SEALED. THE JOINTS IN SHEETED ROOFS SHALL ALSO BE SEALED.

THERMAL INSULATION
INSULATION SHALL COMPLY WITH MINIMUM REQUIRED R-VALUES AND BE INSTALLED SO THAT IT ABUTS OR OVERLAPS ADJOINING INSULATION OR IS SEALED, FORMS A CONTINUOUS BARRIER WITH CEILINGS, WALLS, BULKHEADS OR FLOORS THAT CONTRIBUTE TO THE THERMAL BARRIER AND DOES NOT AFFECT THE SAFE OR EFFECTIVE OPERATION OF ANY SERVICES, INSTALLATION, EQUIPMENT OR FITTING. THERMAL INSULATION MATERIAL SHALL BE EITHER NON-COMBUSTIBLE WHEN TESTED IN ACCORDANCE WITH SANS 10177-5 AND MAY BE INSTALLED IN ALL OCCUPANCY CLASSES OR CLASSIFIED AS COMBUSTIBLE IN ACCORDANCE WITH SANS 10177-5 AND SHALL BE TESTED AND CLASSIFIED IN ACCORDANCE WITH SANS 428 FOR ITS USE AND APPLICATION. REFLECTIVE INSULATION SHALL BE INSTALLED AND SUPPORTED WITH THE NECESSARY AIRSPACE IN ORDER TO ACHIEVE THE REQUIRED R-VALUE BETWEEN A REFLECTIVE SIDE OF THE REFLECTIVE INSULATION AND A BUILDING LINING OR CLADDING, WITH THE REFLECTIVE INSULATION TIGHTLY FITTED AND TAPED AGAINST ANY PENETRATION, DOOR OR WINDOW OPENING AND WITH EACH ADJOINING SHEET OF ROLL MEMBRANE BEING OVERLAPPED BY NOT LESS THAN 100 MM OR TAPED TOGETHER.

GENERAL NOTES:

1. ALL WINDOW AREAS EXCEED 10% OF FLOOR AREA OF WHICH 50%
2. READ FIGURED DIMENSIONS IN PREFERENCE TO SCALING.
3. ALL LEVELS DIMENSIONS, HEIGHTS OF PLINTHS, DEPTHS OF EXCAVATIONS AND NUMBER OF STEPS TO BE FINALLY CHECKED AND DETERMINED BY CONTRACTOR ON SITE.
4. DRAWINGS PREPARED ON BASIS OF SURFACE EXAMINATION ON SITE.
5. RECOMMEND- AB'S OVER ALL WINDOWS AND DOORS WITHOUT FANLIGHTS.
6. RECOMMEND- 2AB'S TO W.C'S BATHROOMS, KITCHENS AND SERVANT'S ROOMS.
7. OBSCURE GLASS TO SERVANTS ROOM W.C'S AND BATHROOMS.
8. ALL HANDRAILS TO BE MIN 1,000MM HIGH, BALUSTERS MAX 100 C/C

BULKED INSULATION IN CEILINGS MAY NOT BE LESS THAT 50mm AGAINST THE WALL WHERE THE IS NO INSULATION IN THE WALL

THERMAL INSULATION MATERIAL TO BE NON COMBUSTIBLE WHEN TESTED IN ACCORDANCE WITH SANS 10177/5 OR CLASSIFIED AS COMBUSTIBLE WITH SANS 10177/5 AND SHALL BE TESTED AND CLASSIFIED IN ACCORDANCE WITH SANS 428FOR IT'S USE AND APPLICATION

REFLECTIVE INSULATION TO BE TIGHTLY FITTED AND TAPED AGAINST ANY PENETRATION, DOOR OR WINDOW OPENING AND WITH EACH ADJOINING SHEET OF ROLL MEMBRANE BEEN OVERLAPPED BY MIN 100mm OR TAPED TOGETHER.

STORE PLAN
SCALE NTS

LAPA PLAN
SCALE NTS

COPYRIGHT NOTICE

Copyright © 2011 (Open Studio Designs cc). Copyright subsists in this drawing. The person or entity whose name appears in the title block of this drawing, is hereby granted a non-exclusive license to use, display, print and / or reproduce this drawing to the extent necessary to carry out and complete the project described in the title block of this drawing.

This license in respect of the copyright is expressly limited as aforesaid and the person and/or entity referred to above shall not be entitled to grant sub-licenses in respect of the copyright in this drawing to any other entity.

This license confers no ownership rights in the copyright vesting in the drawing and this drawing and the copyright subsisting therein will, at all times, remain the property of (Open Studio Design cc).

Any unauthorized reproduction, publication, transmission, adaptation and/or inclusion of this drawing in a cinematograph film or television broadcast is an act of copyright infringement which will render the doer of the act liable for civil law copyright infringement and may in certain circumstances render the doer liable to criminal prosecution.

Requests and enquiries concerning this drawing and the rights subsisting therein should be addressed to the copyright owner.

ACTS OF PARLIAMENT

All Contractors shall ensure that, before any work is put in hand, they comply with all the necessary Acts of Parliament of the Republic of South Africa.