


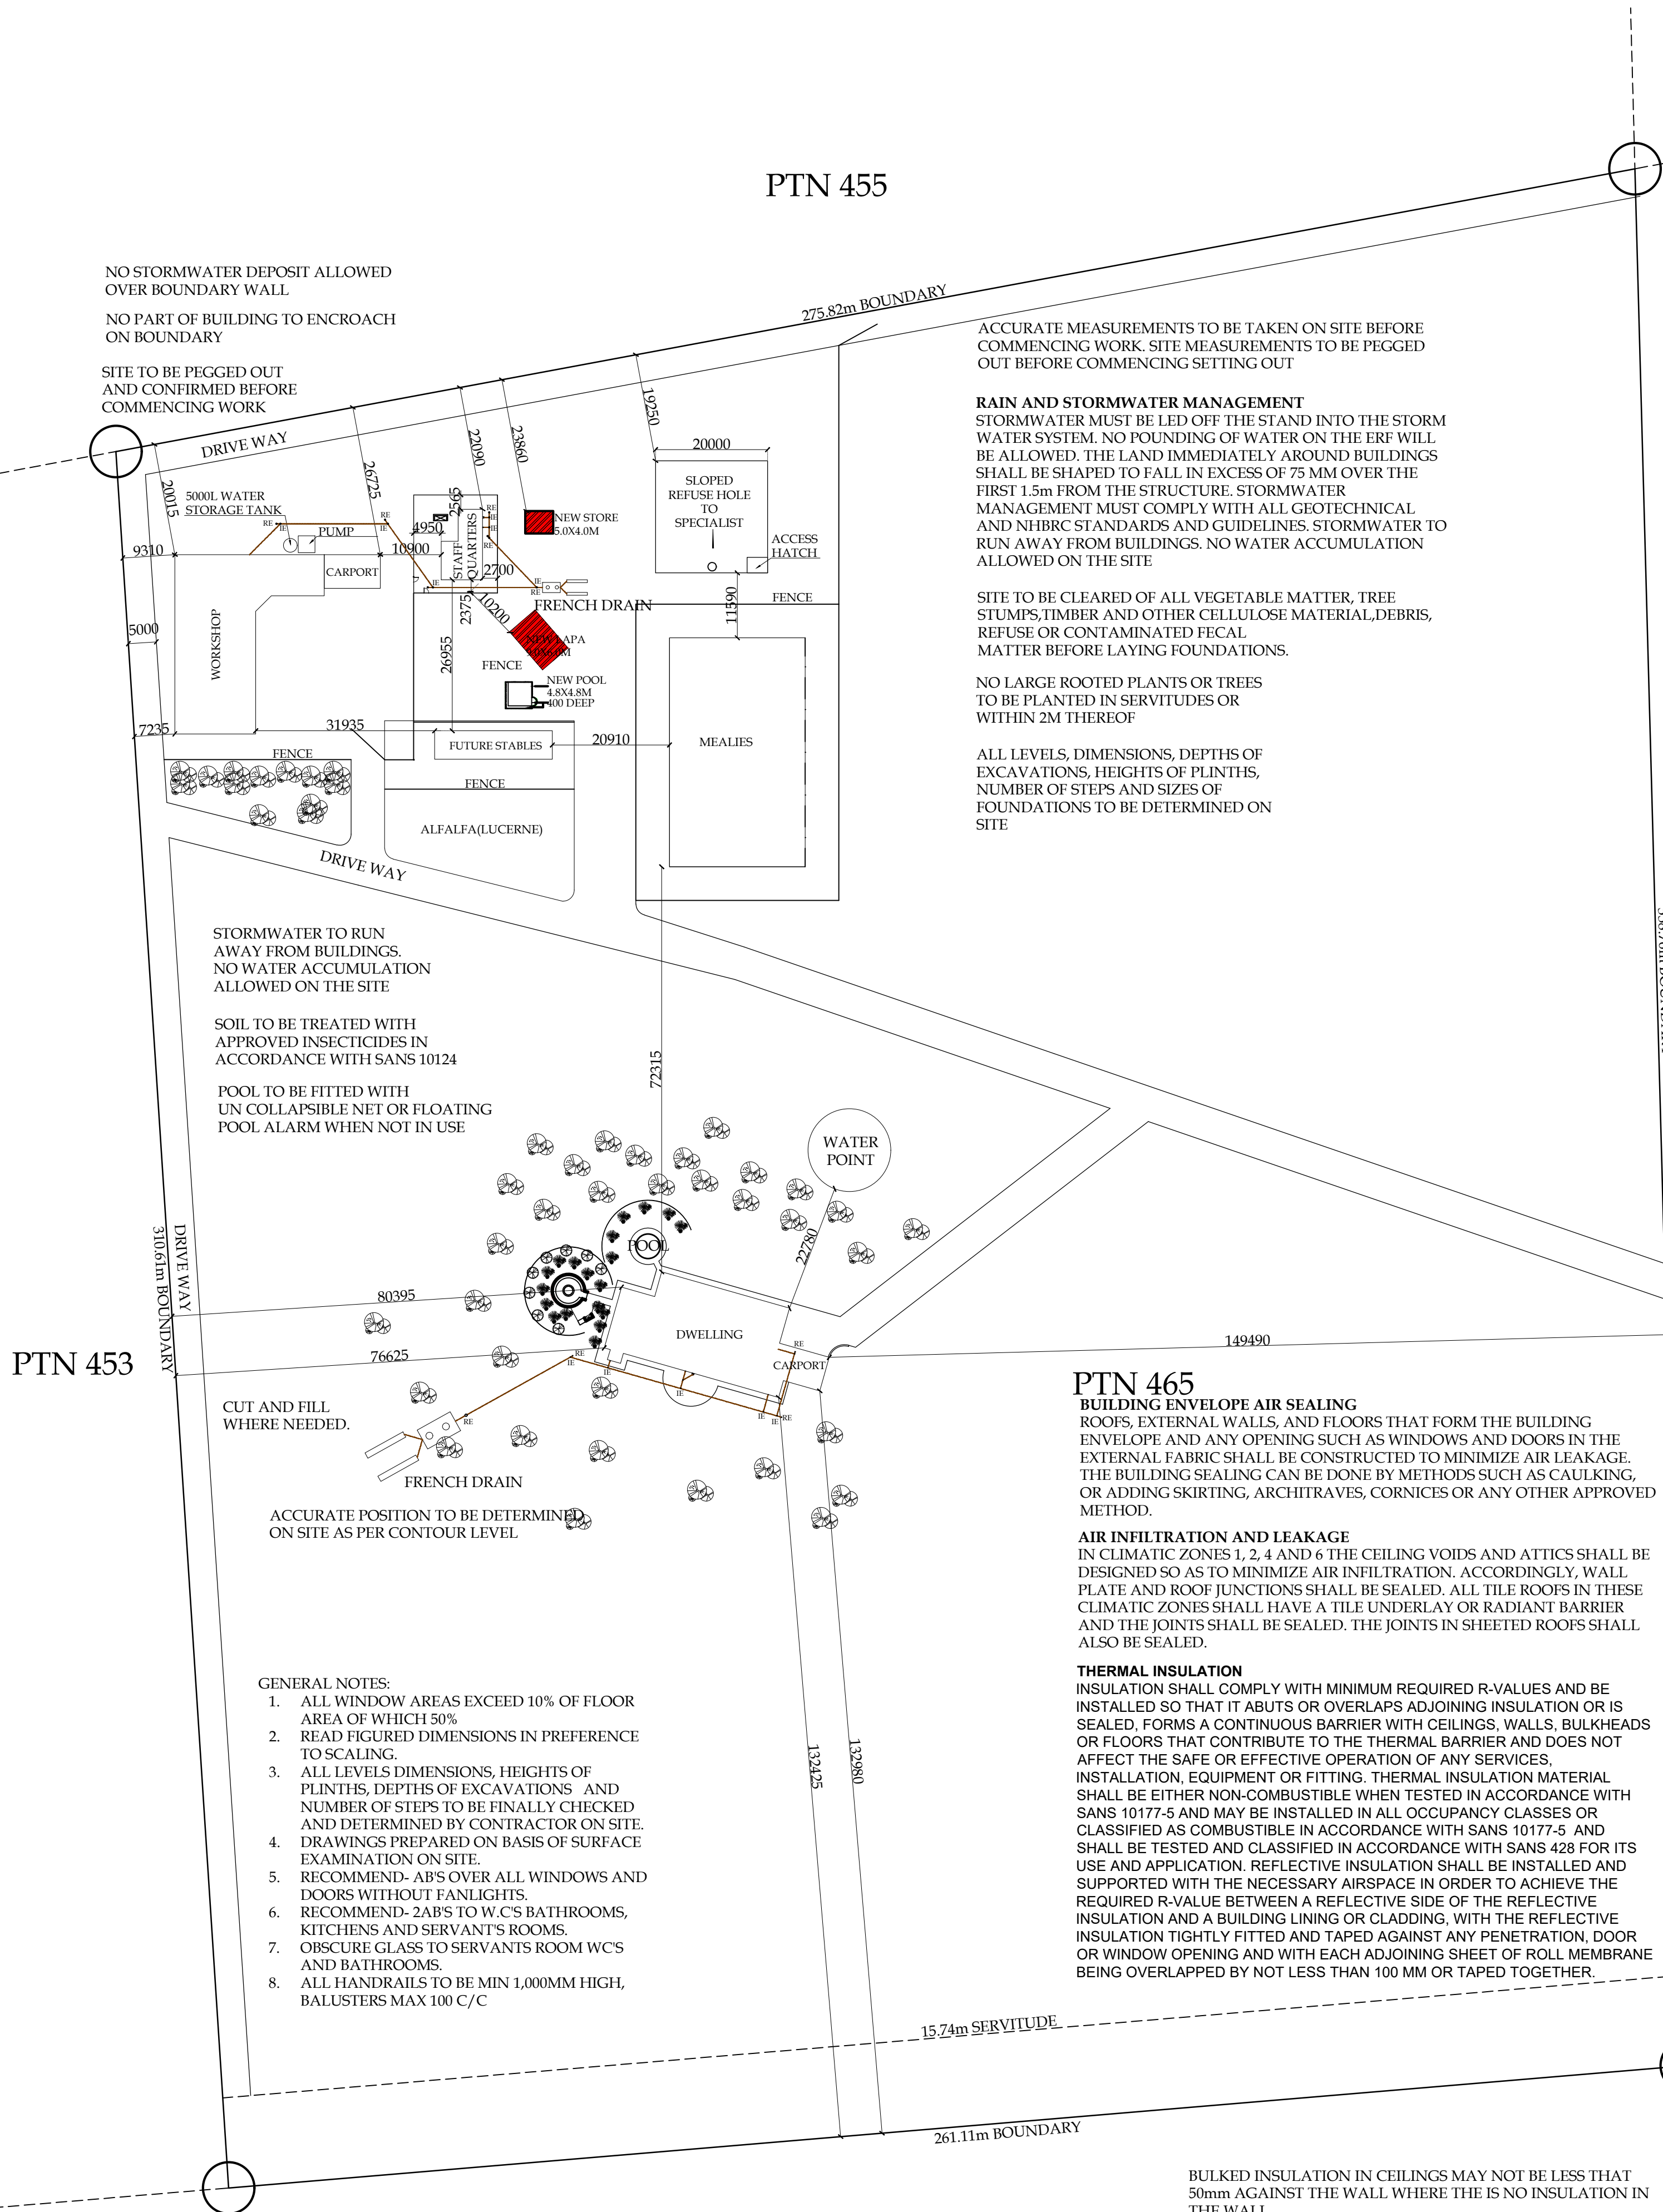

SITE DEVELOPMENT PLAN

SCALE 1:750

PTN 455

KLIPPOORTJIE NO
564-KQ


PTN 465

PTN 466

BULK INSULATION IN CEILINGS MAY NOT BE LESS THAN 50mm AGAINST THE WALL WHERE THE IS NO INSULATION IN THE WALL

THERMAL INSULATION MATERIAL TO BE NON COMBUSTIBLE WHEN TESTED IN ACCORDANCE WITH SANS 10177/5 OR CLASSIFIED AS COMBUSTIBLE WITH SANS 10177/5 AND SHALL BE TESTED AND CLASSIFIED IN ACCORDANCE WITH SANS 428 FOR ITS USE AND APPLICATION

REFLECTIVE INSULATION TO BE TIGHTLY FITTED AND TAPED AGAINST ANY PENETRATION, DOOR OR WINDOW OPENING AND WITH EACH ADJOINING SHEET OF ROLL MEMBRANE BEEN OVERLAPPED BY MIN 100mm OR TAPED TOGETHER.

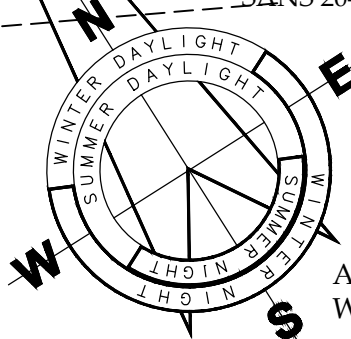

- DRAINAGE NOTES:
1. NO DRAINAGE BENDS OR JUNCTIONS BELOW FLOORS.
 2. BENDS AND JUNCTIONS IN DRAINS TO BE FITTED WITH C.E.S AND I.E'S WITH MARKED COVERS AT GROUND LEVEL.
 3. DRAINS UNDER BUILDINGS TO BE ADEQUATELY PROTECTED AGAINST LOAD.
 4. WASTE PIPES TO HAVE RESEAL TRAPS AND TO BE FULLY ACCESSIBLE OVER FULL LENGTH.
 5. BATH WASTE 50mm INTERNAL DIAMETER BASIN WASTE 50MM INTERNAL DIAMETER.
 6. GULLIES AT KITCHEN TO HAVE CW TAP OVER.
 7. ALL SURFACE PLUMBING TO COMPLY WITH NBR5
 8. GULLY TO BE MIN 85mm ABOVE N.G.L AND NO STORMWATER TO RUN IN OR TO BE DIRECTED TO GULLY
 9. NO GULLY OR MANHOLE ALLOWED UNDER ANY COVERED AND ENCLOSED AREA
 10. VENT PIPES WHERE NEW CLOSED AREAS ARE TO BE CONSTRUCTED MUST BE MOVED OR EXTENDED TO ABOVE THE ROOF IN OPEN VENTILATED AREA
 11. ALL RIS AND IES MUST BE ACCESSIBLE FROM N.G.L

NOTES TO ONE PIPE SYSTEM

- * 500 ELF BOTTLE TRAPS TO WB
- * 500 AAV'S TO SW & B
- * 1100 VV TO WC
- * MIN. INVERT LEVEL : -460mm
- * Ø110 UPVC OVPS
- * FALL OF DRAIN: 1:60 MIN.
- * 1100 PVC SD LAID TO FALL TO MANHOLE - FALL MIN. 1:60

PERMISSIBLE AIR LEAKAGE (AL) IN VEGETATION (TREES, SHRUBS) TO 1) GLAZING AND ROOFLIGHTS

MAXIMUM PERMISSIBLE AL FOR OPENABLE GLAZING SHALL BE 2.0 L/S M2 WITH A PRESSURE DIFFERENCE OF 75 PA, WHEN TESTED IN ACCORDANCE WITH SANS 613.

MAXIMUM PERMISSIBLE AL FOR NON-OPENABLE GLAZING SHALL BE 0.31 L/S M2 WITH A PRESSURE DIFFERENCE OF 75 PA, WHEN TESTED IN ACCORDANCE WITH SANS 613.

FOR GLAZED DOUBLE ACTION SWING DOORS AND REVOLVING DOORS, THE MAXIMUM PERMISSIBLE AL SHALL BE 5.0 L/S M2 WITH A PRESSURE DIFFERENCE OF 75 PA, WHEN TESTED IN ACCORDANCE WITH SANS 613.

2) CHIMNEYS AND FLUES

THE CHIMNEY OR FLUE OF AN OPEN SOLID-FUEL BURNING APPLIANCE SHALL BE PROVIDED WITH A DAMPER OR FLAP THAT CAN BE CLOSED TO SEAL THE CHIMNEY OR FLUE. NOTE A SOLID-FUEL BURNING DEVICE IS A HEATER THAT BURNS MATERIAL SUCH AS TIMBER OR COAL. THIS DOES NOT APPLY TO GAS AND LIQUID FUEL BURNING DEVICES.

3) ROOF LIGHTS AND SKYLIGHTS

ROOF LIGHTS AND SKYLIGHTS SHALL BE SEALED, OR BE CAPABLE OF BEING SEALED TO MINIMIZE AL. ROOF LIGHTS AND SKYLIGHTS SHALL BE CONSTRUCTED WITH A COMPRESSIBLE SEAL IF THEY ARE OPENABLE.

4) EXTERNAL DOORS

A SEAL TO RESTRICT AL SHALL BE FITTED TO EACH EDGE OF AN EXTERNAL DOOR AND OTHER SUCH OPENING THAT SERVES A CONDITIONED SPACE OR A HABITABLE ROOM IN CLIMATIC ZONES 1, 2, 4 AND 6 AS PER SANS 204. THE SEAL MAY BE A FOAM OR RUBBER COMPRESSIBLE STRIP OR A FIBROUS SEAL. EXTERNAL SWING DOORS SHALL BE FITTED WITH A DRAUGHT PROTECTION DEVICE TO THE BOTTOM EDGE ON EACH LEAF.

5) EXHAUST FANS

AN EXHAUST FAN SHALL BE FITTED WITH A SEALING DEVICE SUCH AS A SELF-CLOSING DAMPER OR FILTER WHEN SERVING A CONDITIONED SPACE OR A HABITABLE ROOM IN CLIMATIC ZONES 1, 2, 4 AND 6 AS PER SANS 204.


6) ROOFS, WALLS AND FLOORS

ROOFS, EXTERNAL WALLS, EXTERNAL FLOORS AND ANY OPENING SUCH AS GLAZING OR DOOR IN THE EXTERNAL FABRIC SHALL BE CONSTRUCTED TO MINIMIZE AIR LEAKAGE IN ACCORDANCE WITH 4.4.1 OF SANS 204 WHEN FORMING PART OF THE EXTERNAL FABRIC OF A CONDITIONED SPACE OR A HABITABLE ROOM IN CLIMATIC ZONES 1, 2, 4 AND 6 AS PER SANS 204.

ARCHITECTURAL DRAWINGS TO BE READ IN CONJUNCTION WITH ENGINEERING DRAWINGS


FLOORS, WALLS, GEYSER PIPES AND ROOFS TO BE INSULATED IN ACCORDANCE WITH SANS 10400

BUILDING MUST BE IN ACCORDANCE WITH THE APPROVED BUILDING PLAN. NO CHANGES MAY BE MADE TO SUCH PLANS WITHOUT THE EXPRESSED CONSENT OF THE AUTHOR OF SUCH DOCUMENT

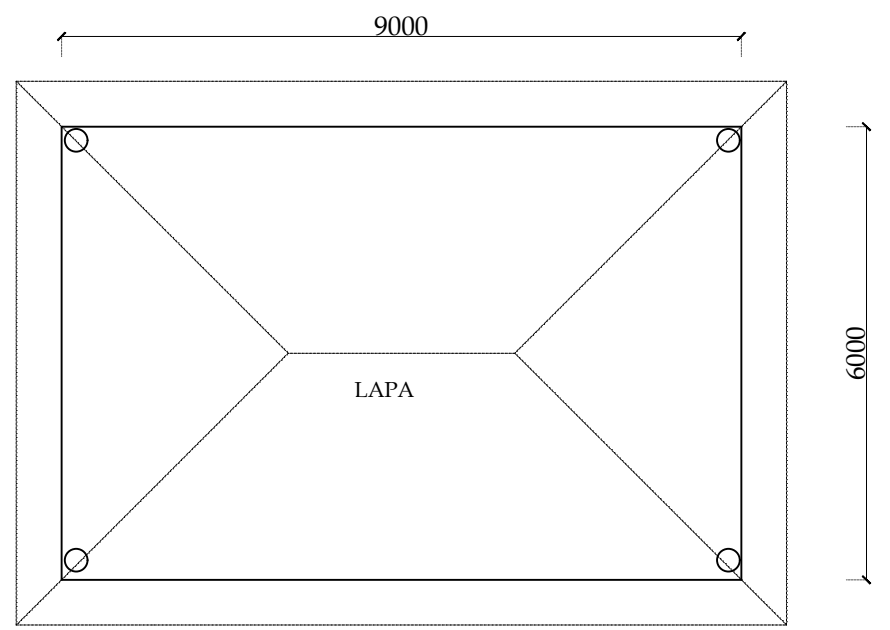

LAPA PLAN

SCALE NTS

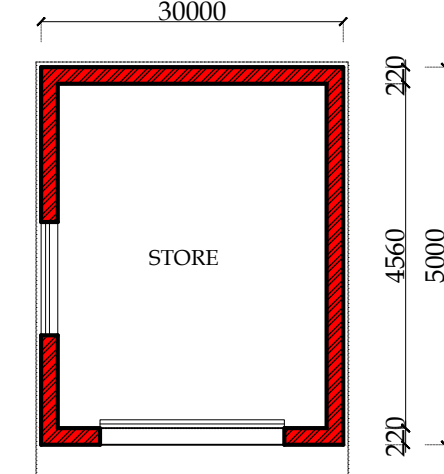

RAMP OR DRIVEWAY USED BY MOTOR VEHICLES SHALL HAVE A GRADIENT OF NOT MORE THAN 1 IN 25 WITHIN A DISTANCE OF 5m FROM ANY STREET BOUNDARY CROSSED BY SUCH RAMP OR DRIVEWAY. RAMP OR DRIVEWAY USED BY PEDESTRIANS OTHER THAN THOSE RAMPS OR DRIVEWAYS PROVIDED FOR THE USE OF PERSONS IN WHEELCHAIRS, SHALL HAVE A GRADIENT OF NOT MORE THAN 1 IN 8. RAMP PROVIDED FOR THE USE OF PERSONS IN WHEELCHAIRS SHALL BE IN ACCORDANCE WITH THE REQUIREMENTS OF SANS 10400-S AND RAMP DESIGNED FOR USE BY BOTH VEHICLES AND PEDESTRIANS SHALL HAVE A WALKWAY NOT LESS THAN 1.2m WIDE WHICH SHALL BE PROVIDED WITH A KERB NOT LESS THAN 150mm HIGH.

ALL REINFORCED CONCRETE SLABS, FOUNDATIONS, COLUMN DETAILS, BEAMS, STAIRS AND RETAINING WALLS TO BE BUILT STRICTLY IN ACCORDANCE WITH ENGINEERS DETAIL AND UNDER HIS SUPERVISION

ALL DIMENSIONS TO BE MEASURED OUT AND PEGGED ON SITE BEFORE COMMENCING WORK

Copyright © 2011 (Open Studio Designs cc). Copyright subsists in this drawing. The person or entity whose name appears in the title block of this drawing, is hereby granted a non-exclusive license to use, display, print and / or reproduce this drawing to the extent necessary to carry out and complete the project described in the title block of this drawing.

This license in respect of the copyright is expressly limited as aforesaid and the person and/or entity referred to above shall not be entitled to grant sub-licenses in respect of the copyright in this drawing to any other entity.

This license confers no ownership rights in the copyright vesting in the drawing and this drawing and the copyright subsisting therein will, at all times, remain the property of (Open Studio Design cc).

Any unauthorized reproduction, publication, transmission, adaptation and/or inclusion of this drawing in a cinematograph film or television broadcast is an act of copyright infringement which will render the doer of the act liable for civil law copyright infringement and may in certain circumstances render the doer liable to criminal prosecution.

Requests and enquiries concerning this drawing and the rights subsisting therein should be addressed to the copyright owner.

ACTS OF PARLIAMENT

All Contractors shall ensure that, before any work is put in hand, they comply with all the necessary Acts of Parliament of the Republic of South Africa.

SITE AREA 86 680m²

AREA SCHEDULE

GROUND STOREY:		
DWELLING UNIT	=	458.46m ²
WORKSHOP/STORE ROOMS	=	555.64m ²
CARPORT	=	131.64m ²
STAFF ROOMS	=	75.37m ²

TOTAL GROUND STOREY: 1221.11m²

NEW FLOOR AREA: 1221.11m²

TOTAL NEW COVERAGE 1221.11m²

NEW LAPA = 54.00m²

NEW STORE = 20.00m²

NEW ADDITIONS: 74.00m²

TOTAL NEW COVERAGE 1295.11m²

COVERAGE:	
PROVIDED	1.5%
FAR:	
PROVIDED	0.015

GENERAL NOTES:

QUALITY OF ALL MATERIALS AND WORKMANSHIP TO COMPLY WITH THE RELEVANT S.A.B.S. SPECIFICATION AND SHALL COMPLY WITH THE MINIMUM STANDARD SPECIFIED IN THE STANDARD PREAMBLES IN THE BILL OF QUANTITIES OR, IN THE ABSENCE OF A BILL OF QUANTITIES, AVAILABLE FOR PERUSAL AT THE OFFICES OF THE ARCHITECTS. THE CONTRACTOR IS RESPONSIBLE FOR CORRECT SETTING OUT OF THE BUILDINGS, ALL EXTERNAL AND ALL INTERNAL WALLS WITH PARTICULAR REFERENCE TO BOUNDARIES, BUILDING LINES, ETC.

THE CONTRACTOR IS TO VERIFY LEVELS, HEIGHTS AND DIMENSIONS ON SITE AND TO CHECK SAME AGAINST THE DRAWINGS BEFORE PUTTING ANY WORK IN HAND. ANY DISCREPANCIES FROM THE THEORETICAL TO BE BROUGHT TO THE ARCHITECT'S ATTENTION.

THE CONTRACTOR AND ALL SUB-CONTRACTORS ARE TO CHECK THE DETAILS SHOWN ON THIS DRAWING FOR COMPLIANCE WITH STANDARDS OF BEST BUILDING PRACTICE (WHICH IS WHAT IS EXPECTED TO BE DELIVERED) WITH PARTICULAR REFERENCE TO SPECIAL REQUIREMENTS NECESSITATED BY LOCAL AND/OR ON SITE CONDITIONS AND TO REPORT ANY COMMENT TO THE ARCHITECTS.

THE CONTRACTOR IS TO LOCATE AND IDENTIFY EXISTING SERVICES ON SITE AND TO PROTECT THESE FROM DAMAGE THROUGHOUT THE DURATION OF THE WORKS.


ANY ERRORS, DISCREPANCIES OR OMISSIONS ON THIS DRAWING ARE TO BE REPORTED TO THE ARCHITECT IMMEDIATELY.

THE CONTRACTOR IS TO BUILD IN APPROVED DPCS, WHETHER OR NOT THESE ARE SHOWN ON DRAWINGS, TO ALL EXTERNAL WALLS AT EACH FLOOR, BEAM OR PARAPET LEVEL, AND TO ALL WINDOWS, DOORS, GRILLES OR OTHER OPENING IN EXTERNAL WALLS. CAVITY WALLS TO HAVE STEPPED DPCS.

ANY QUERIES ARISING FROM THE ABOVE MUST BE REPORTED TO THE ARCHITECT FOR CLARIFICATION BEFORE ANY WORK IS PUT IN HAND.

THIS DRAWING IS NOT TO BE SCALED. FIGURES TO BE USED AT ALL TIMES, WHERE FIGURED DIMENSIONS ARE GIVEN, THIS MUST BE CONFIRMED BY THE ARCHITECT.

BURNT CLAY BRICKS IN COMPLIANCE WITH THE RELEVANT S.A.B.S. CODE ONLY SHALL BE USED UNLESS SPECIFIC APPROVAL IS OBTAINED FROM THE ARCHITECT FOR THE USE OF ALTERNATIVE TYPE OF BRICK.

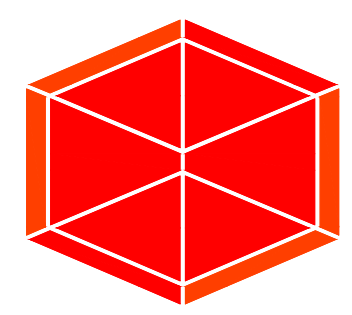

Open Studio Designs
Architectural & Interiors

Mobile 083-306-4315
Fax-086-643-8765
openstudio.design@gmail.com

PROPOSED REVISED SITE PLAN ON PTN 465 OF THE FARM KROMDRAAI 560KQ

CLIENT:	
TECHNOLOGIST: REG. NO:	W JUNG-KRUGER D 0573

DATE: JULY 18	DWG NO:
DRAWN: WJK	SHEET: 1 OF 1