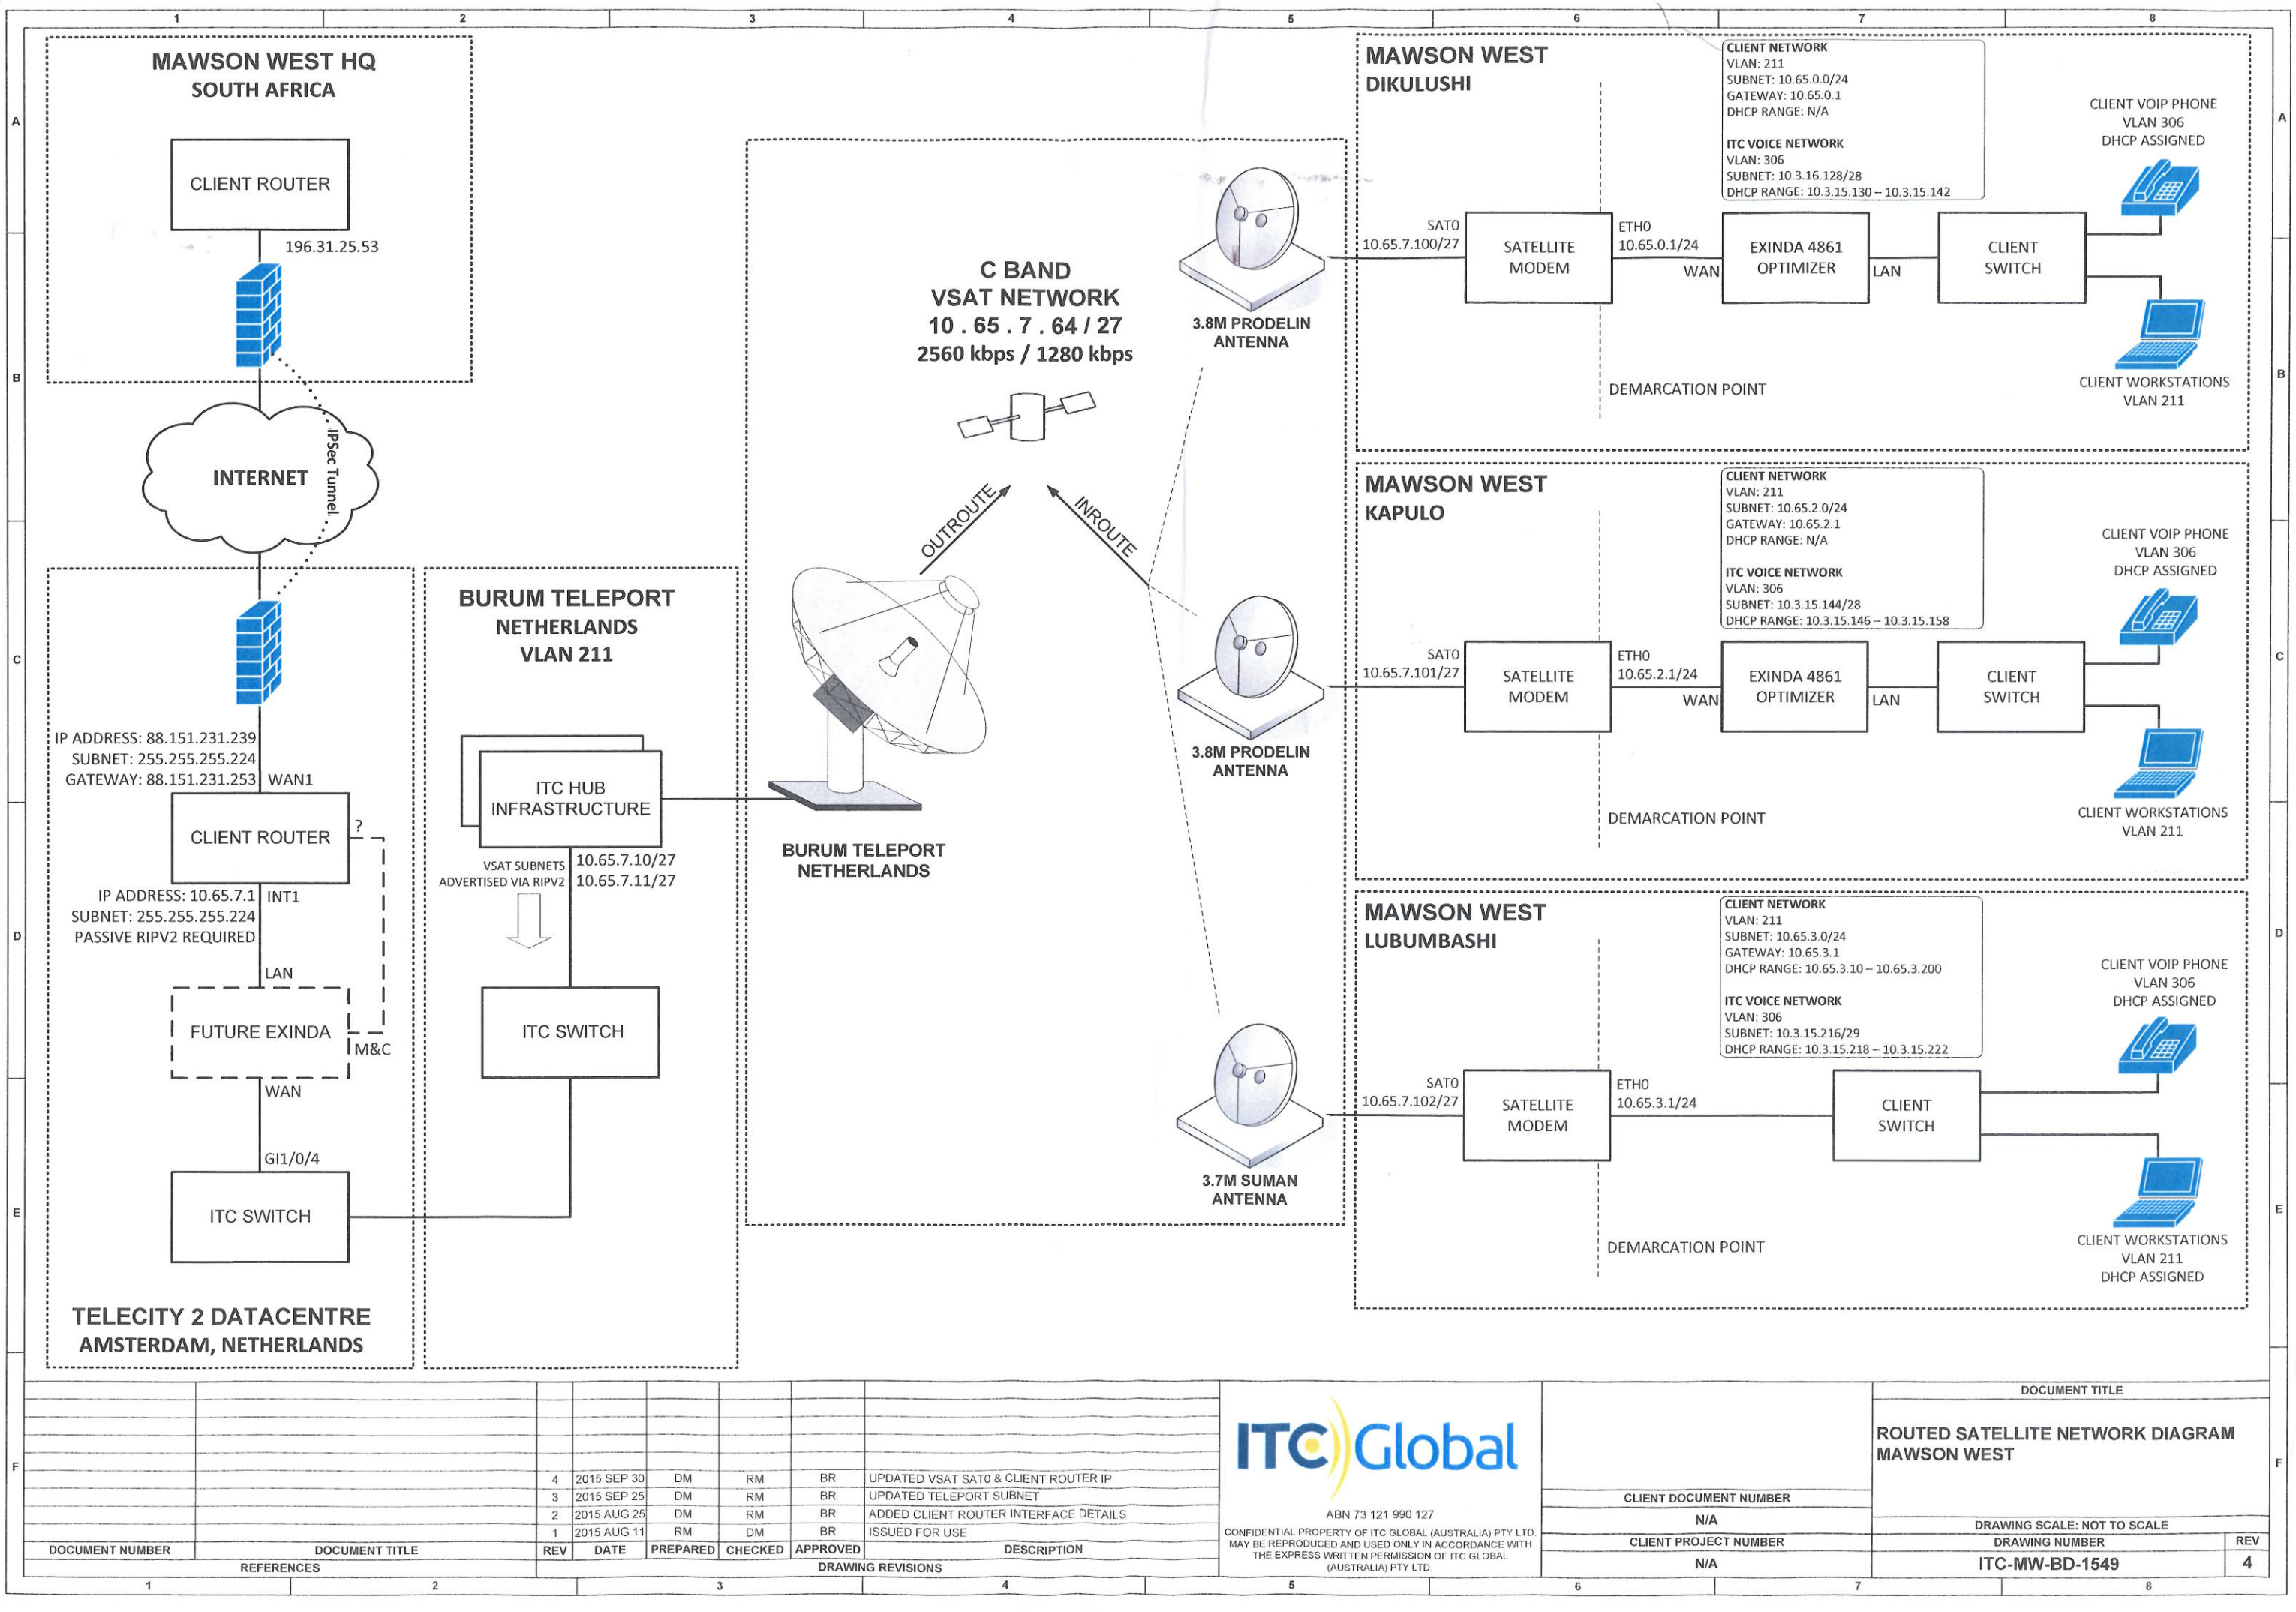

REV	DATE	PREPARED	CHECKED	APPROVED	DESCRIPTION
4	2015 SEP 30	DM	RM	BR	UPDATED VSAT SAT0 & CLIENT ROUTER IP
3	2015 SEP 25	DM	RM	BR	UPDATED TELEPORT SUBNET
2	2015 AUG 25	DM	RM	BR	ADDED CLIENT ROUTER INTERFACE DETAILS
1	2015 AUG 11	RM	DM	BR	ISSUED FOR USE

DRAWING REVISIONS

REFERENCES

DOCUMENT NUMBER | DOCUMENT TITLE

ITC Global

ABN 73 121 990 127

CONFIDENTIAL PROPERTY OF ITC GLOBAL (AUSTRALIA) PTY LTD. MAY BE REPRODUCED AND USED ONLY IN ACCORDANCE WITH THE EXPRESS WRITTEN PERMISSION OF ITC GLOBAL (AUSTRALIA) PTY LTD.

CLIENT DOCUMENT NUMBER: N/A

CLIENT PROJECT NUMBER: N/A

DOCUMENT TITLE

ROUTED SATELLITE NETWORK DIAGRAM MAWSON WEST

DRAWING SCALE: NOT TO SCALE

DRAWING NUMBER: ITC-MW-BD-1549

REV: 4